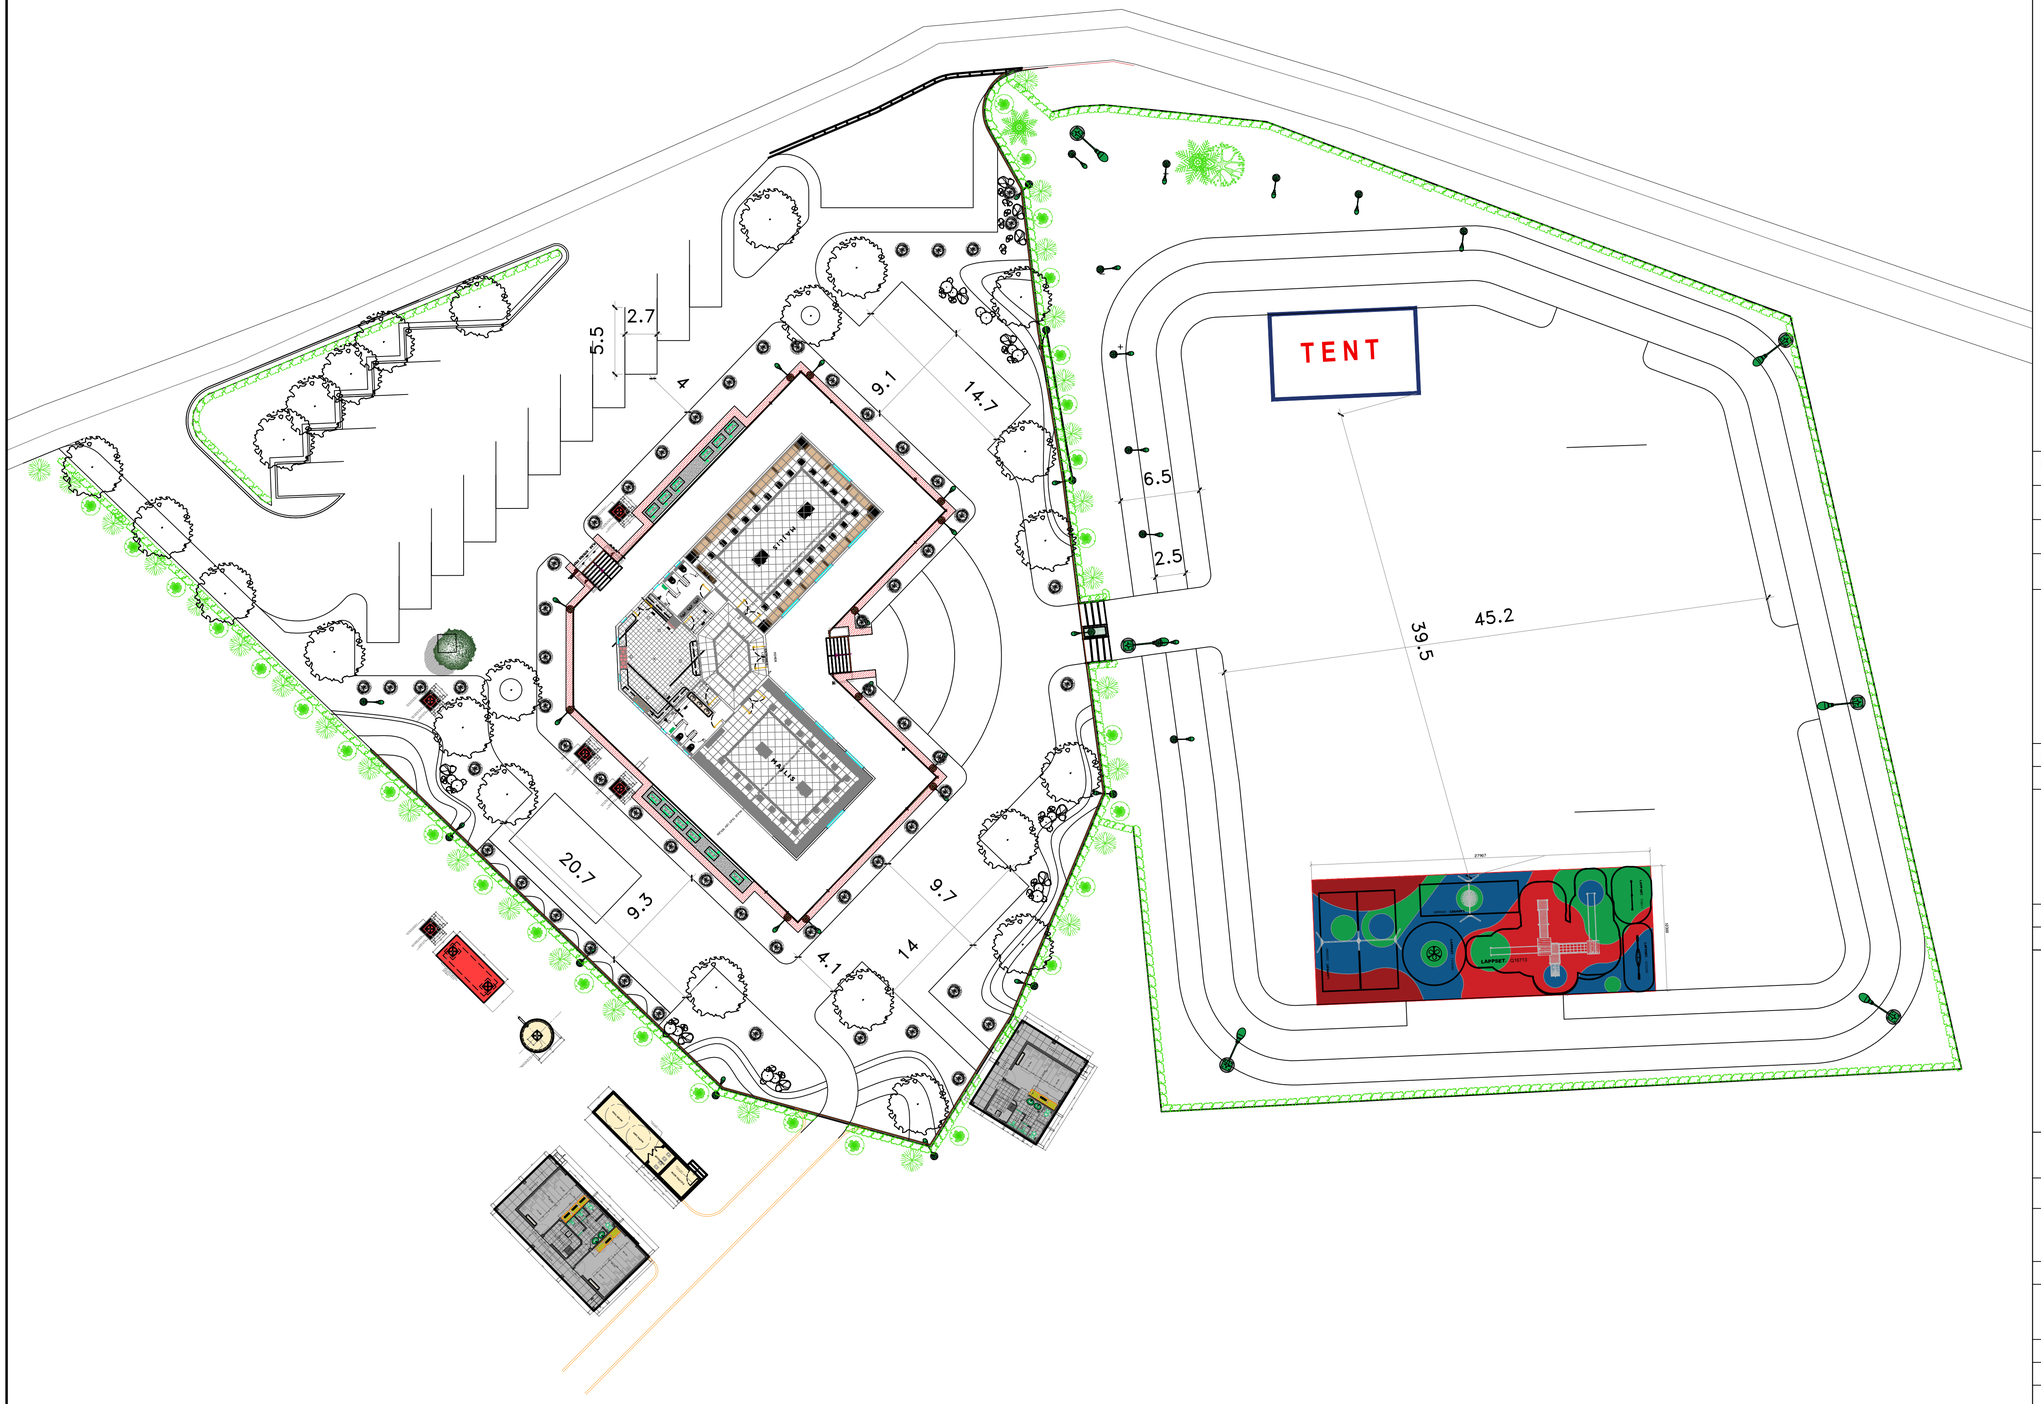


REVISION NO:	DATE:	DESCRIPTION:	BY:
0	16-Aug-2023	FOR APPROVAL	SEC

U.D.D STAMP	MUNICIPALITY STAMP

INQUIRY NO. : ****	APPLICATION NO. : 20230801
CONSULTANT REG. **** GRADE: A	SUB-CONSULTANT REG. NO. * GRADE: *
CONSULTANT STAMP & SIGNATURE :	SUB-CONSULTANT & SIGNATURE :
TECHNICAL MANAGER :	TECHNICAL MANAGER :
REGISTRATION NO.:	REGISTRATION NO.:

HTA Construction & Trading

PROJECT:	AL-MAJED FARM
LOCATION:	RAWDET RASHED
CLIENT:	AL MAJED FARM
DATE : 26-AUG-2023	JOB NO:
TITLE:	LANDSCAPE PLAN LAYOUT
DRAWING NO: SSP-SW1	SCALE: AS SHOWN
DRAWN BY: Ar.SHAREEF / DESIGNED BY: Arch. M.S / CHECKED BY: Arch. M.S	
CAD FILE: 00-00 / REGISTRATION NO: / REGISTRATION NO:	
REVISION: 00 / SIGNATURE: / SIGNATURE:	